



C
T
H
E
S
E
I
D
E
A
S
,
P
L
A
N
S
,
&
D
E
S
I
G
N
S
M
A
Y
N
O
T
B
E
R
E
P
R
O
D
U
C
E
D
O
R
C
O
P
I
E
D
I
N
A
N
Y
F
O
R
M
W
I
T
H
O
U
T
T
H
E
E
X
P
R
E
S
S
O
F
C
I
C
.
D
I
M
E
N
S
I
O
N
S
S
H
O
W
N
O
N
T
H
E
S
E
D
R
A
W
I
N
G
S
S
U
P
E
R
S
E
D
E
S
C
A
L
E
D
I
M
E
N
S
I
O
N
S

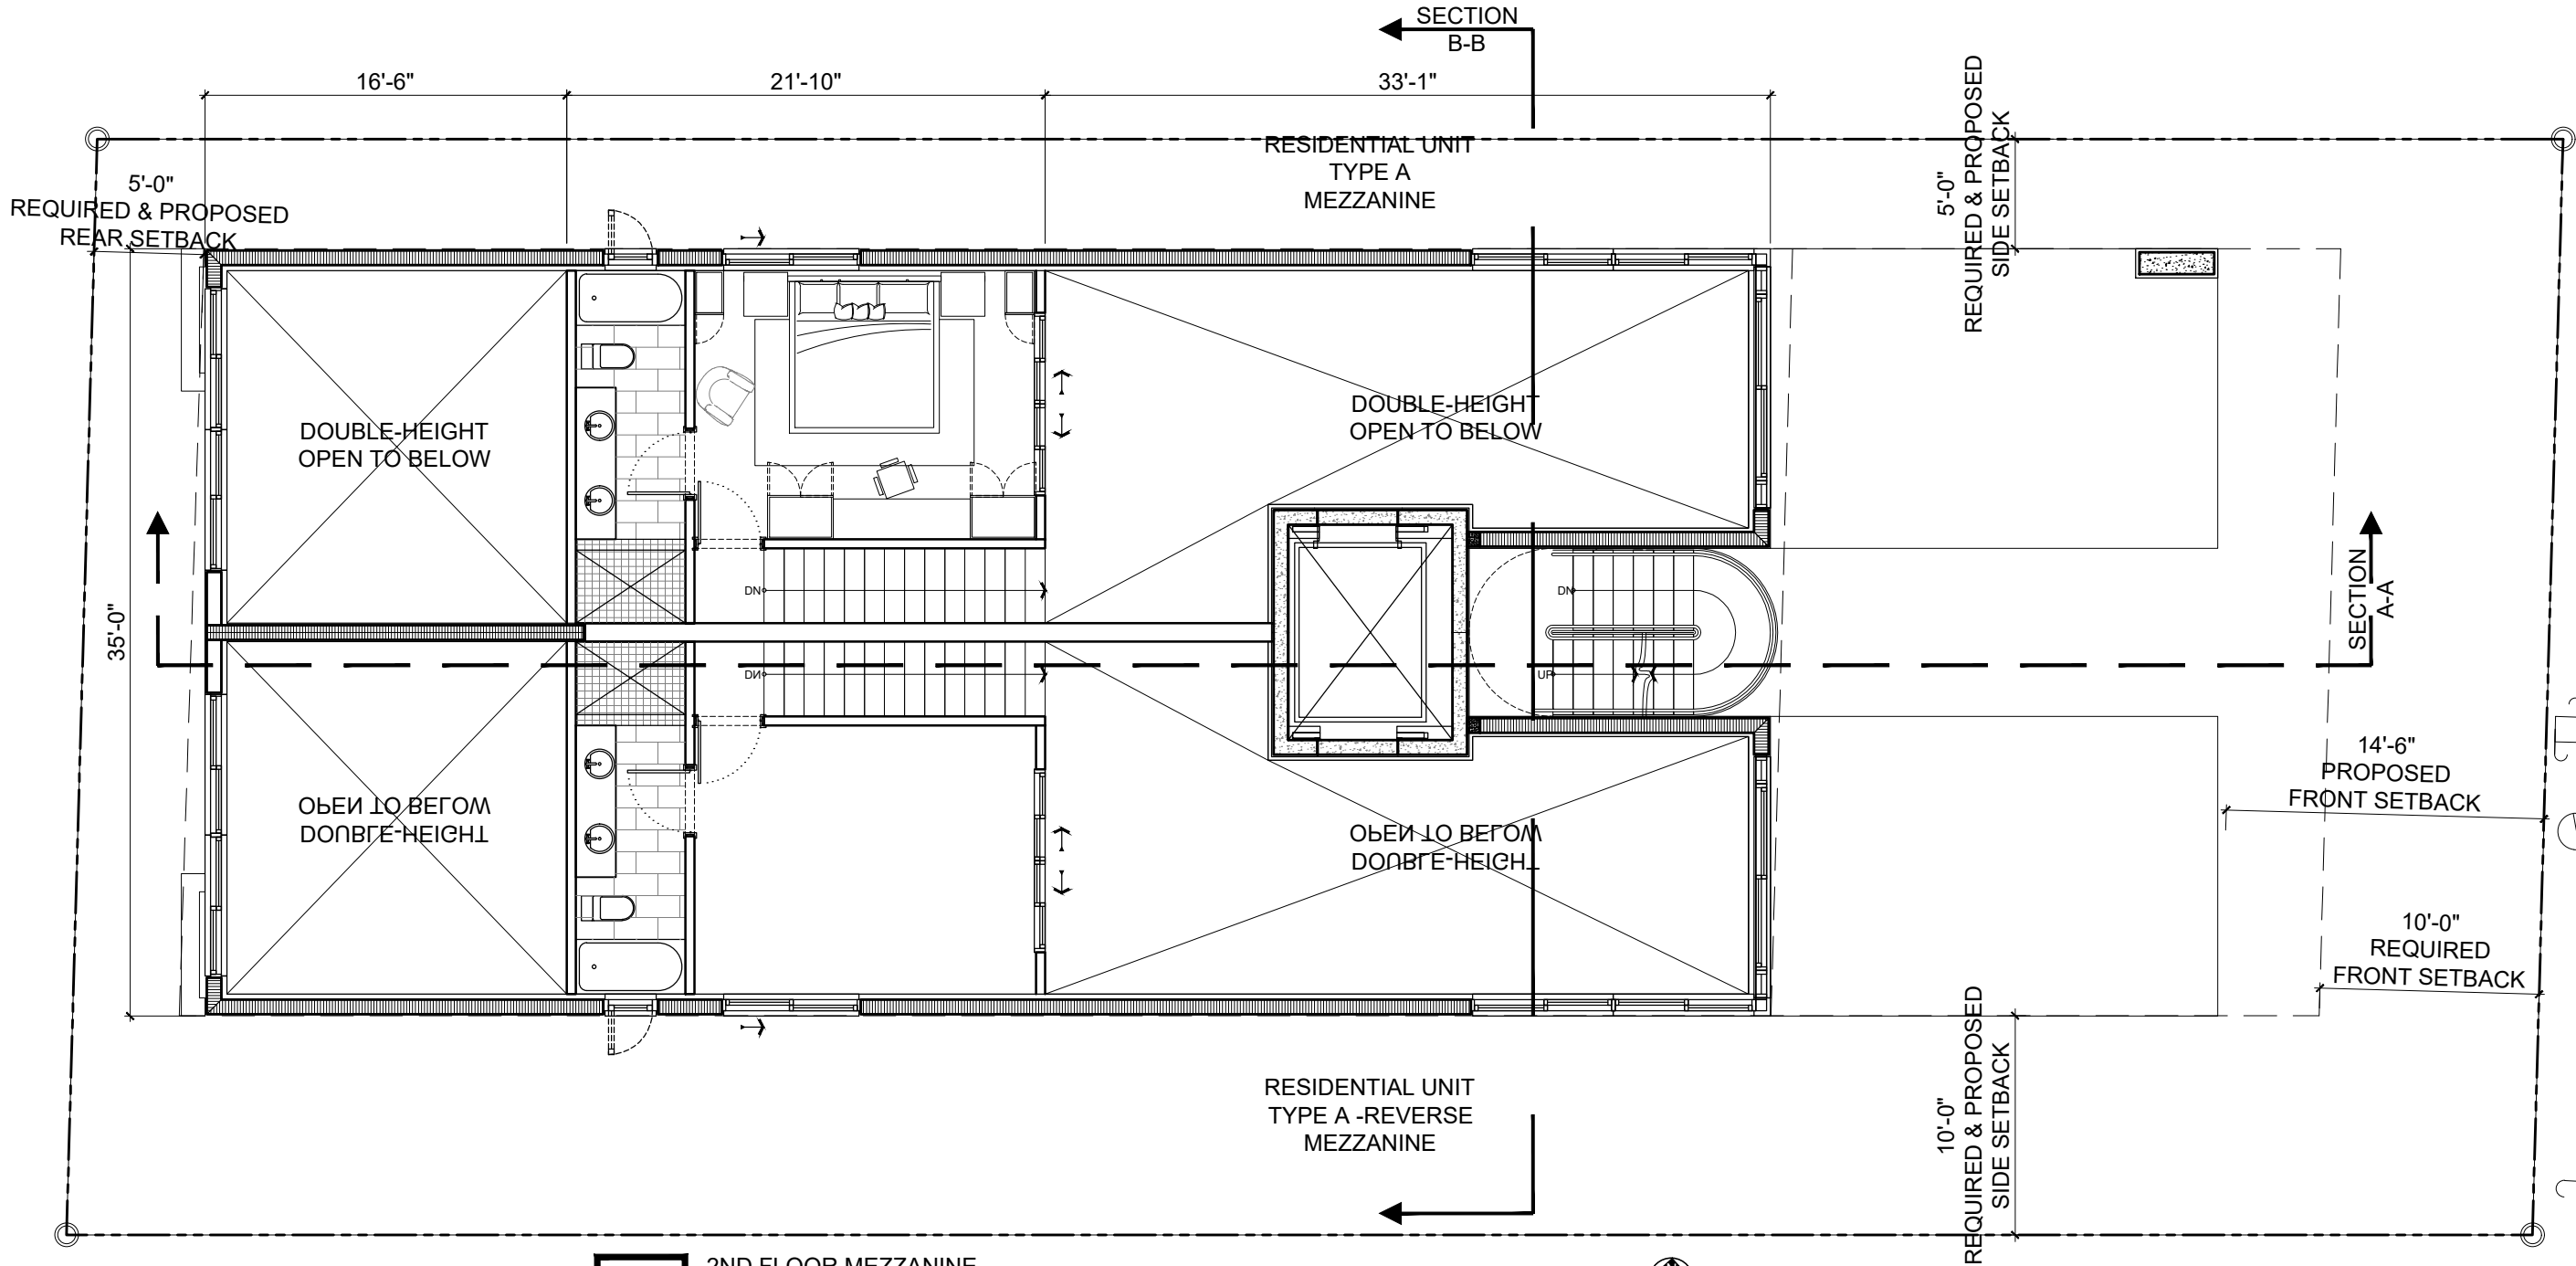

1 2ND FLOOR MEZZANINE
SCALE: 1/8" = 1'-0"

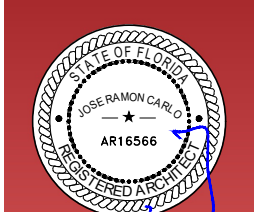

CARLO INTERNATIONAL CONSULTING
ARCHITECTURE
INTERIOR DESIGN
REAL ESTATE ADVISORY

JOSE R. CARLO
FL LICENSE NO.: AR-16566
11 ISLAND AVENUE #2105
MIAMI BEACH FL 33139
(305) 490-0493
JCARLO@CIC-ARCHITECTURE.COM

LULLABY CONDOMINIUM RESIDENCES
7928 BYRON AVENUE, MIAMI BEACH, FL 33141
DESIGN DEVELOPMENT

20 MAY 2026

PROJECT :	2501	
DATE :	MAY 20, 2026	
FILE :	7928B DD 260519	
REV.	DESCRIPTION	DATE

SCALE: AS NOTED

2ND FLOOR MEZZANINE

A2.2a